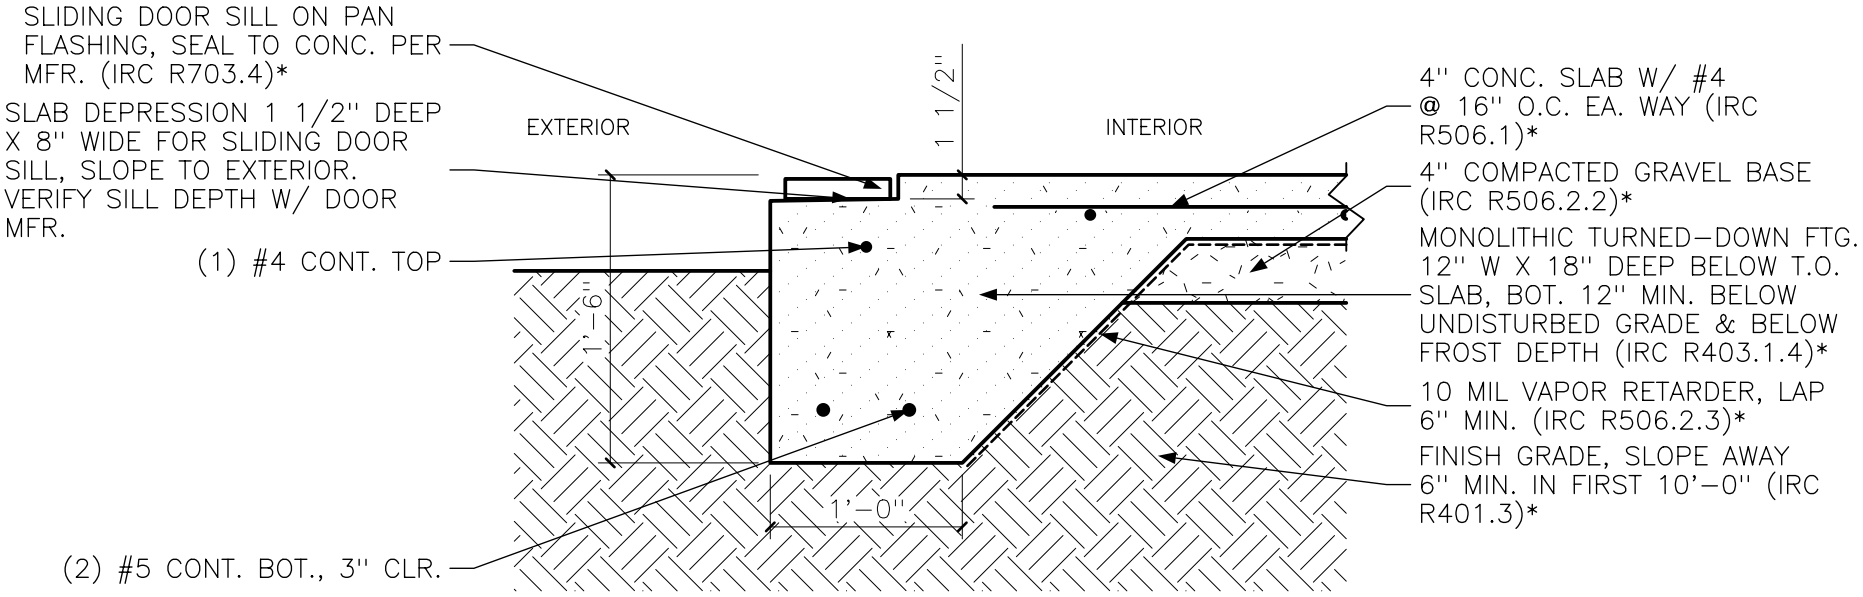


2 / S-501

SLAB EDGE AT SLIDING DOOR

SCALE: 1" = 1'-0"

DETAIL	PROJECT	SCALE	DRAWN	DATE	DETAIL NO
SLAB EDGE AT SLIDING DOOR		1" = 1'-0"	KERF REFERENCE	2026-10-05	2/S-501