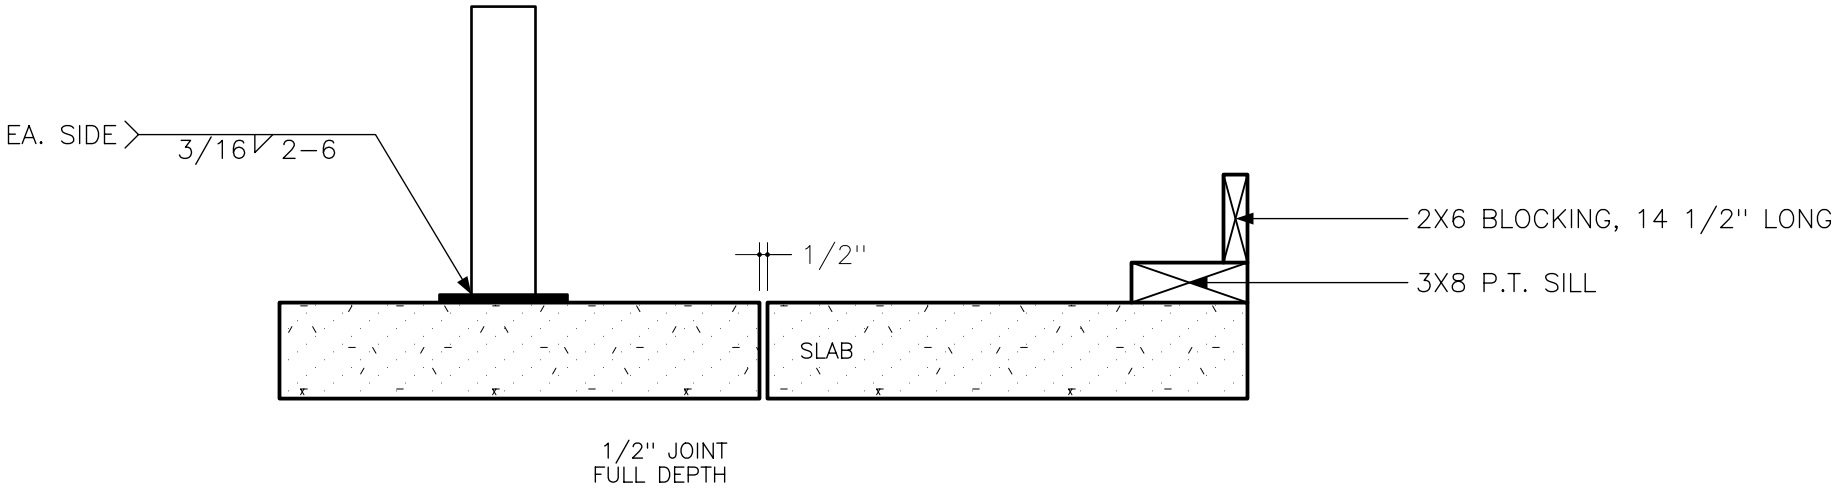


1

SLAB JOINT, 3X SILL AND STEEL POST WELDED TO EMBED PLATE

SCALE: 1" = 1'-0"

DETAIL	PROJECT	SCALE	DRAWN	DATE	DETAIL NO
SLAB JOINT, 3X SILL AND STEEL POST WELDED TO EMBED PLATE		1" = 1'-0"	KERF		1