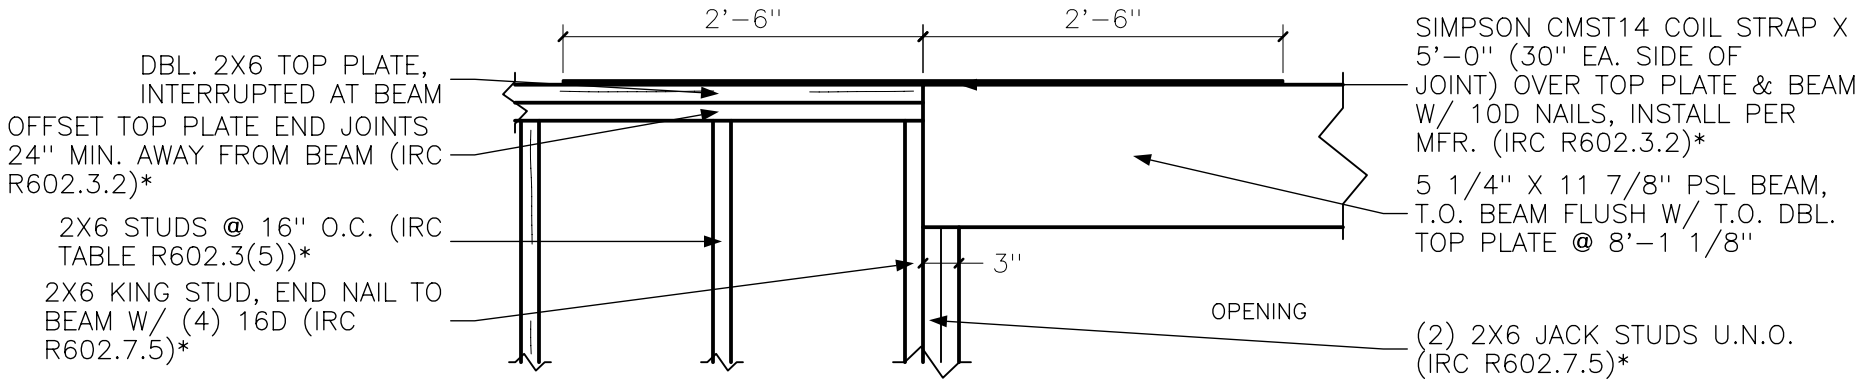


1

FLUSH PSL BEAM AT 2X6 TOP PLATE – ELEVATION

SCALE: 3/4" = 1'–0"

DETAIL	PROJECT	SCALE	DRAWN	DATE	DETAIL NO
FLUSH PSL BEAM AT 2X6 TOP PLATE – ELEVATION		3/4" = 1'–0"	KERF	2026–10–06	1