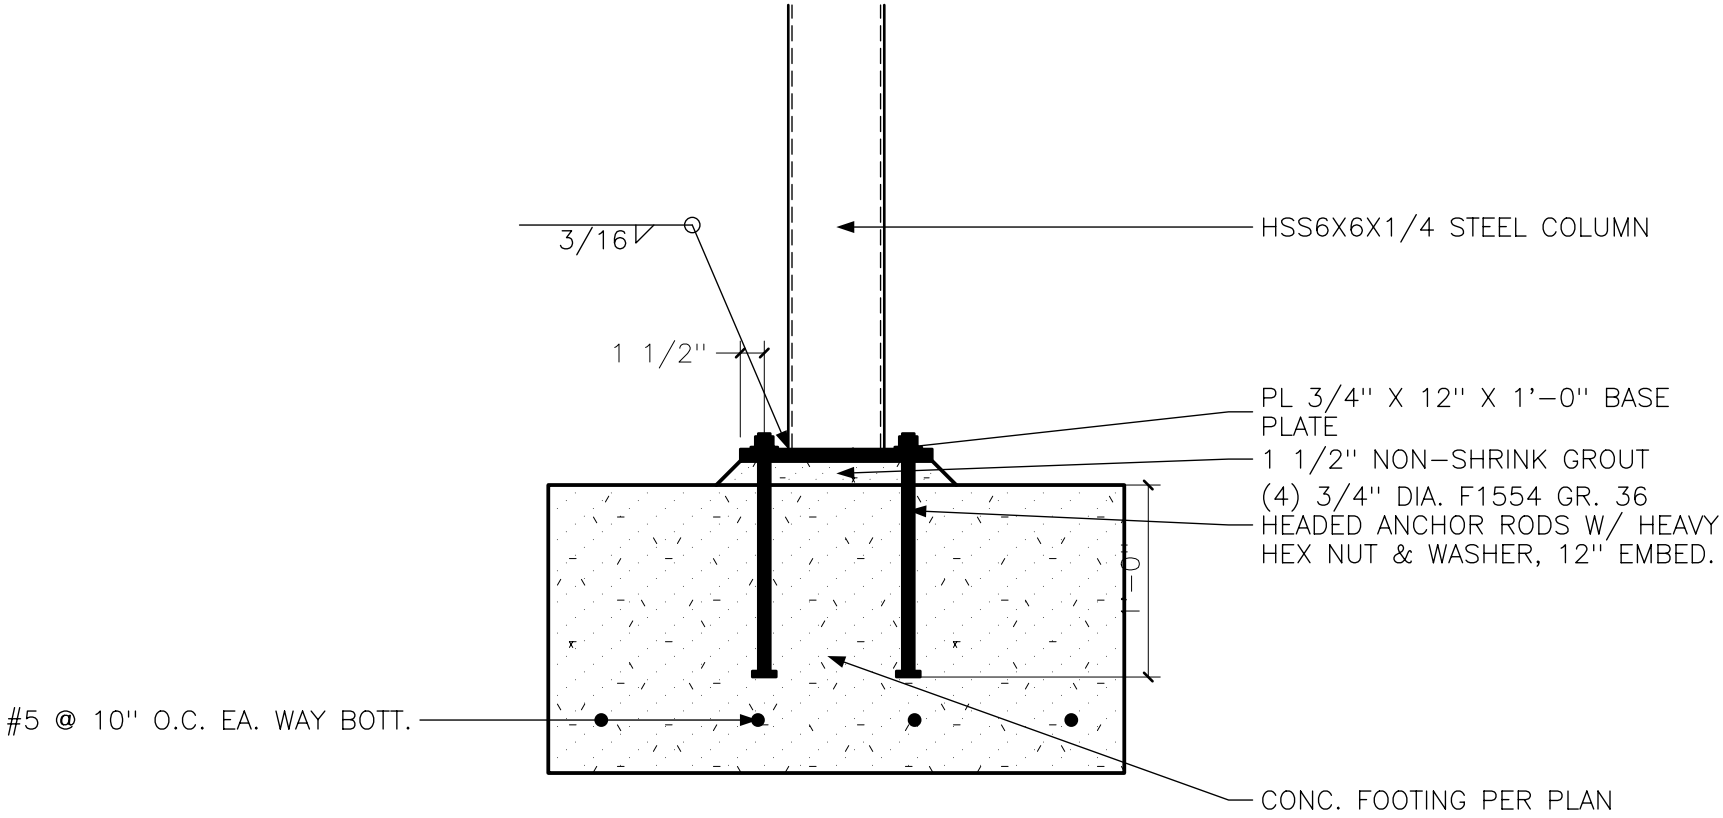


1 / S-503

HSS COLUMN BASE PLATE AT FOOTING

SCALE: 1" = 1'-0"

DETAIL	PROJECT	SCALE	DRAWN	DATE	DETAIL NO
HSS COLUMN BASE PLATE AT FOOTING		1" = 1'-0"	KERF REFERENCE	2026-10-31	1/S-503