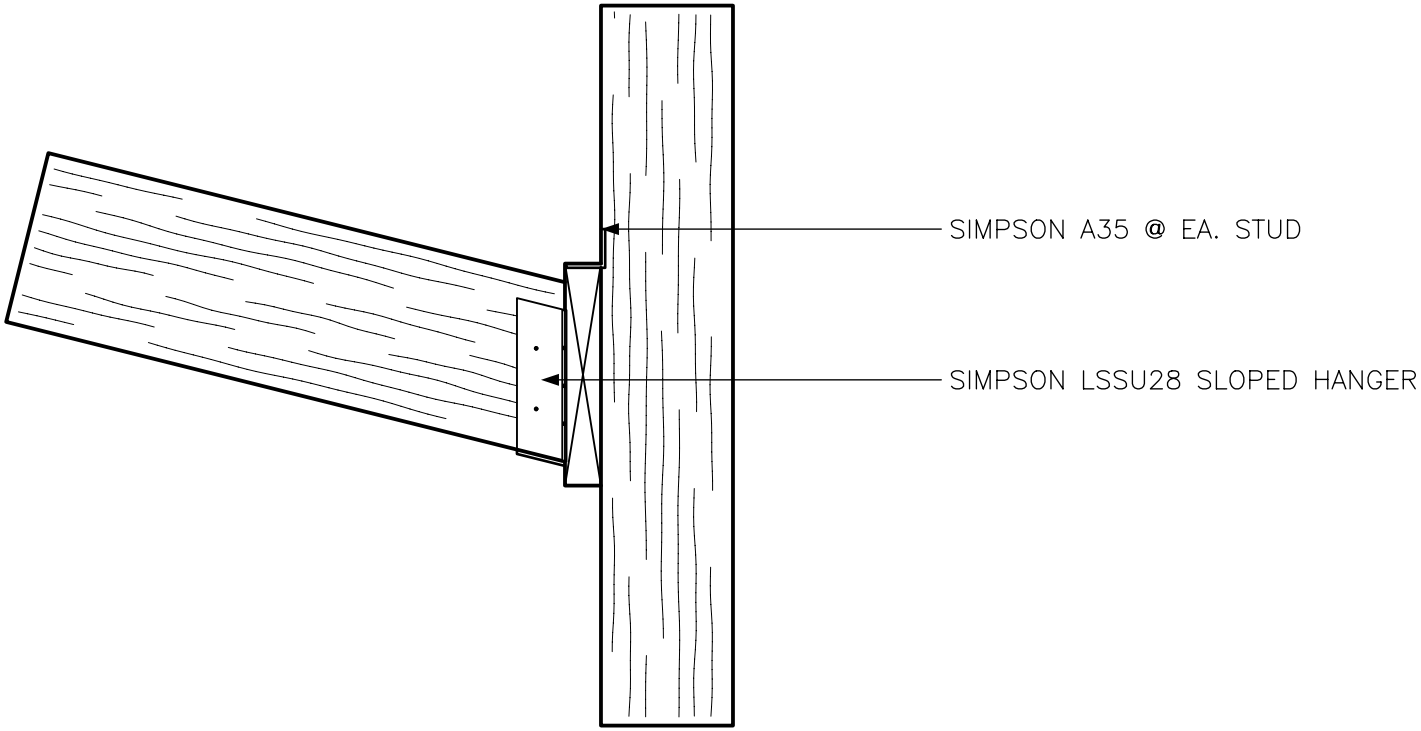


2

SLOPED HANGER AND A35 AT LEDGER

SCALE: 1 1/2" = 1'-0"

DETAIL	PROJECT	SCALE	DRAWN	DATE	DETAIL NO
SLOPED HANGER AND A35 AT LEDGER		1 1/2" = 1'-0"	KERF		2