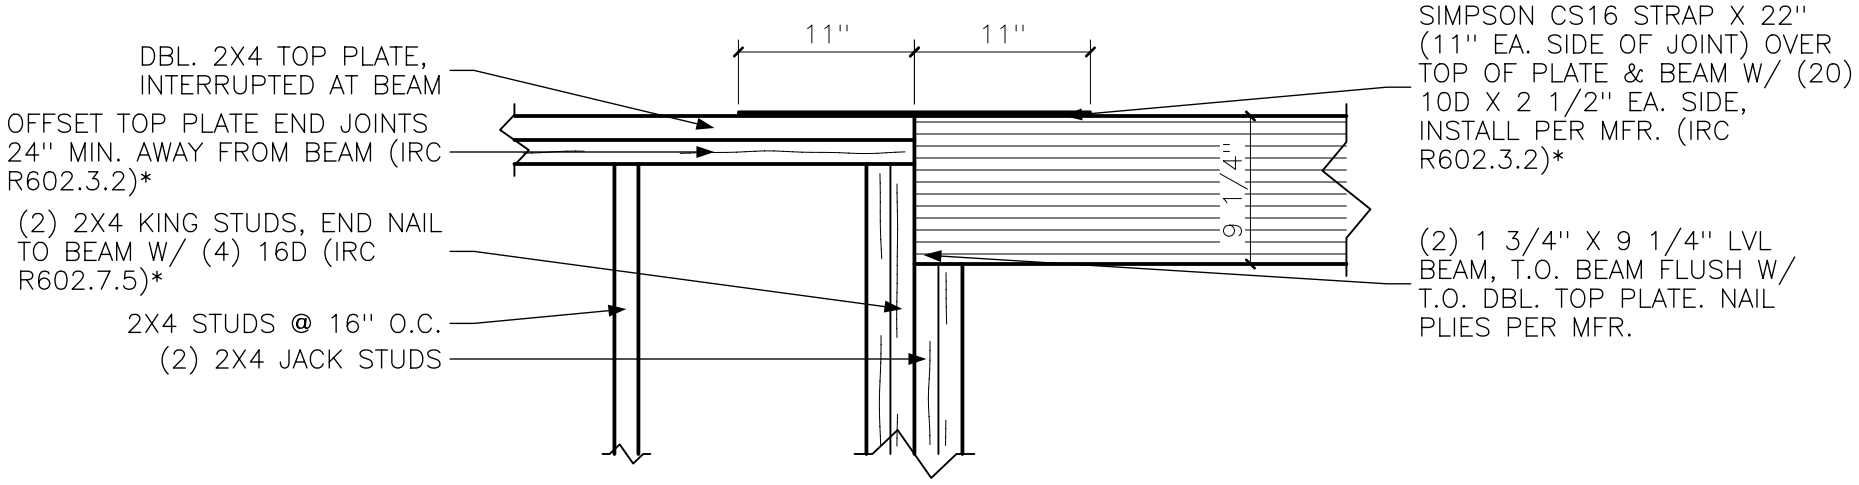


1
S-502

FLUSH BEAM AT TOP PLATE – ELEVATION

SCALE: 1'' = 1'–0''

DETAIL	PROJECT	SCALE	DRAWN	DATE	DETAIL NO
FLUSH BEAM AT TOP PLATE – ELEVATION		1'' = 1'–0''	KERF REFERENCE	2026–10–05	1/S–502