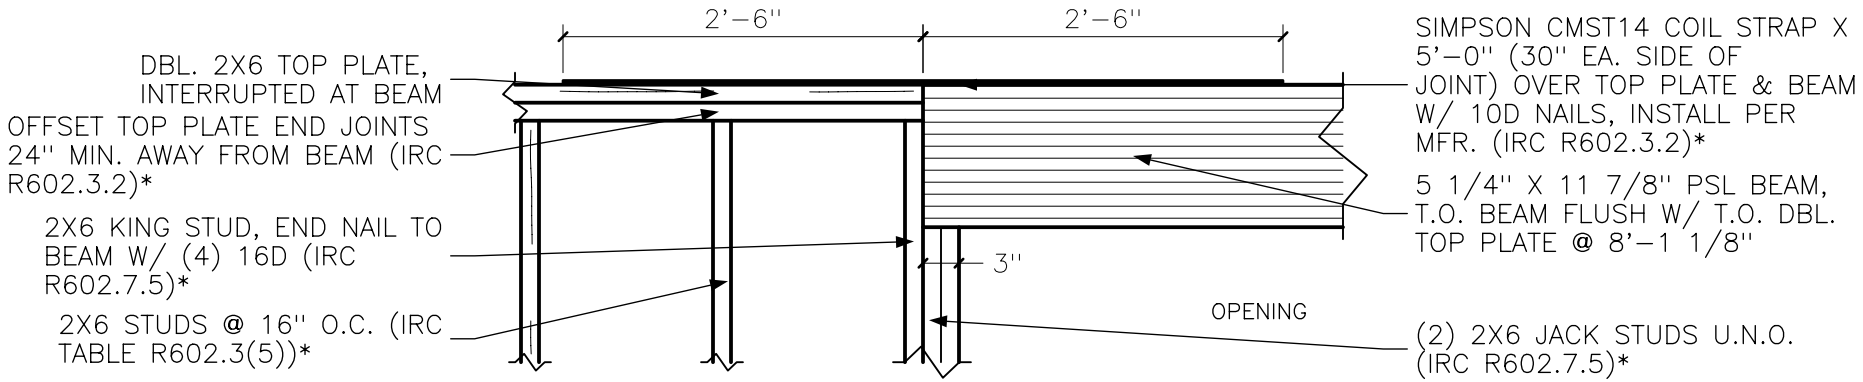


1

FLUSH PSL BEAM AT 2X6 TOP PLATE – ELEVATION

SCALE: 3/4" = 1'–0"

DETAIL	PROJECT	SCALE	DRAWN	DATE	DETAIL NO
FLUSH PSL BEAM AT 2X6 TOP PLATE – ELEVATION		**3/4" = 1'–0"**	KERF	**2026–10–06**	1