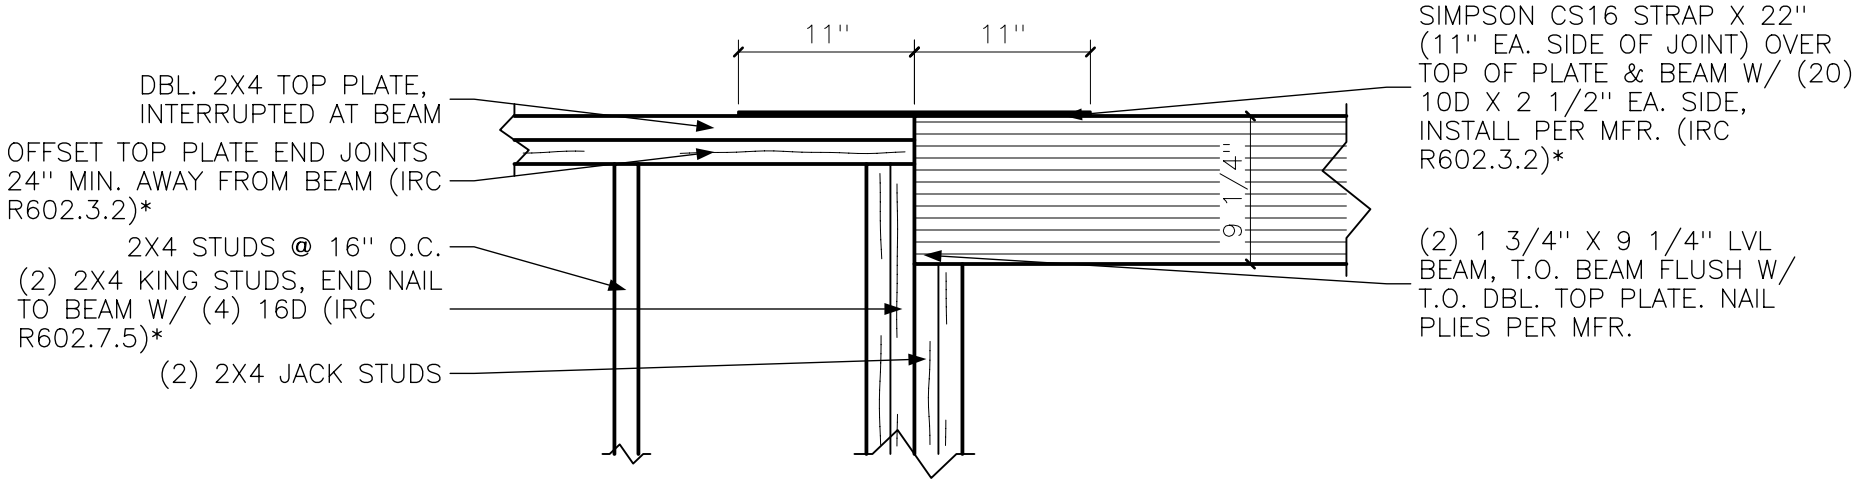



1 / S-502

## FLUSH BEAM AT TOP PLATE – ELEVATION

SCALE: 1'' = 1'–0''

| DETAIL | PROJECT | SCALE | DRAWN | DATE | DETAIL NO |
|---|---|---|---|---|---|
| FLUSH BEAM AT TOP PLATE – ELEVATION | | 1'' = 1'–0'' | KERF REFERENCE | 2026–10–05 | 1/S–502 |