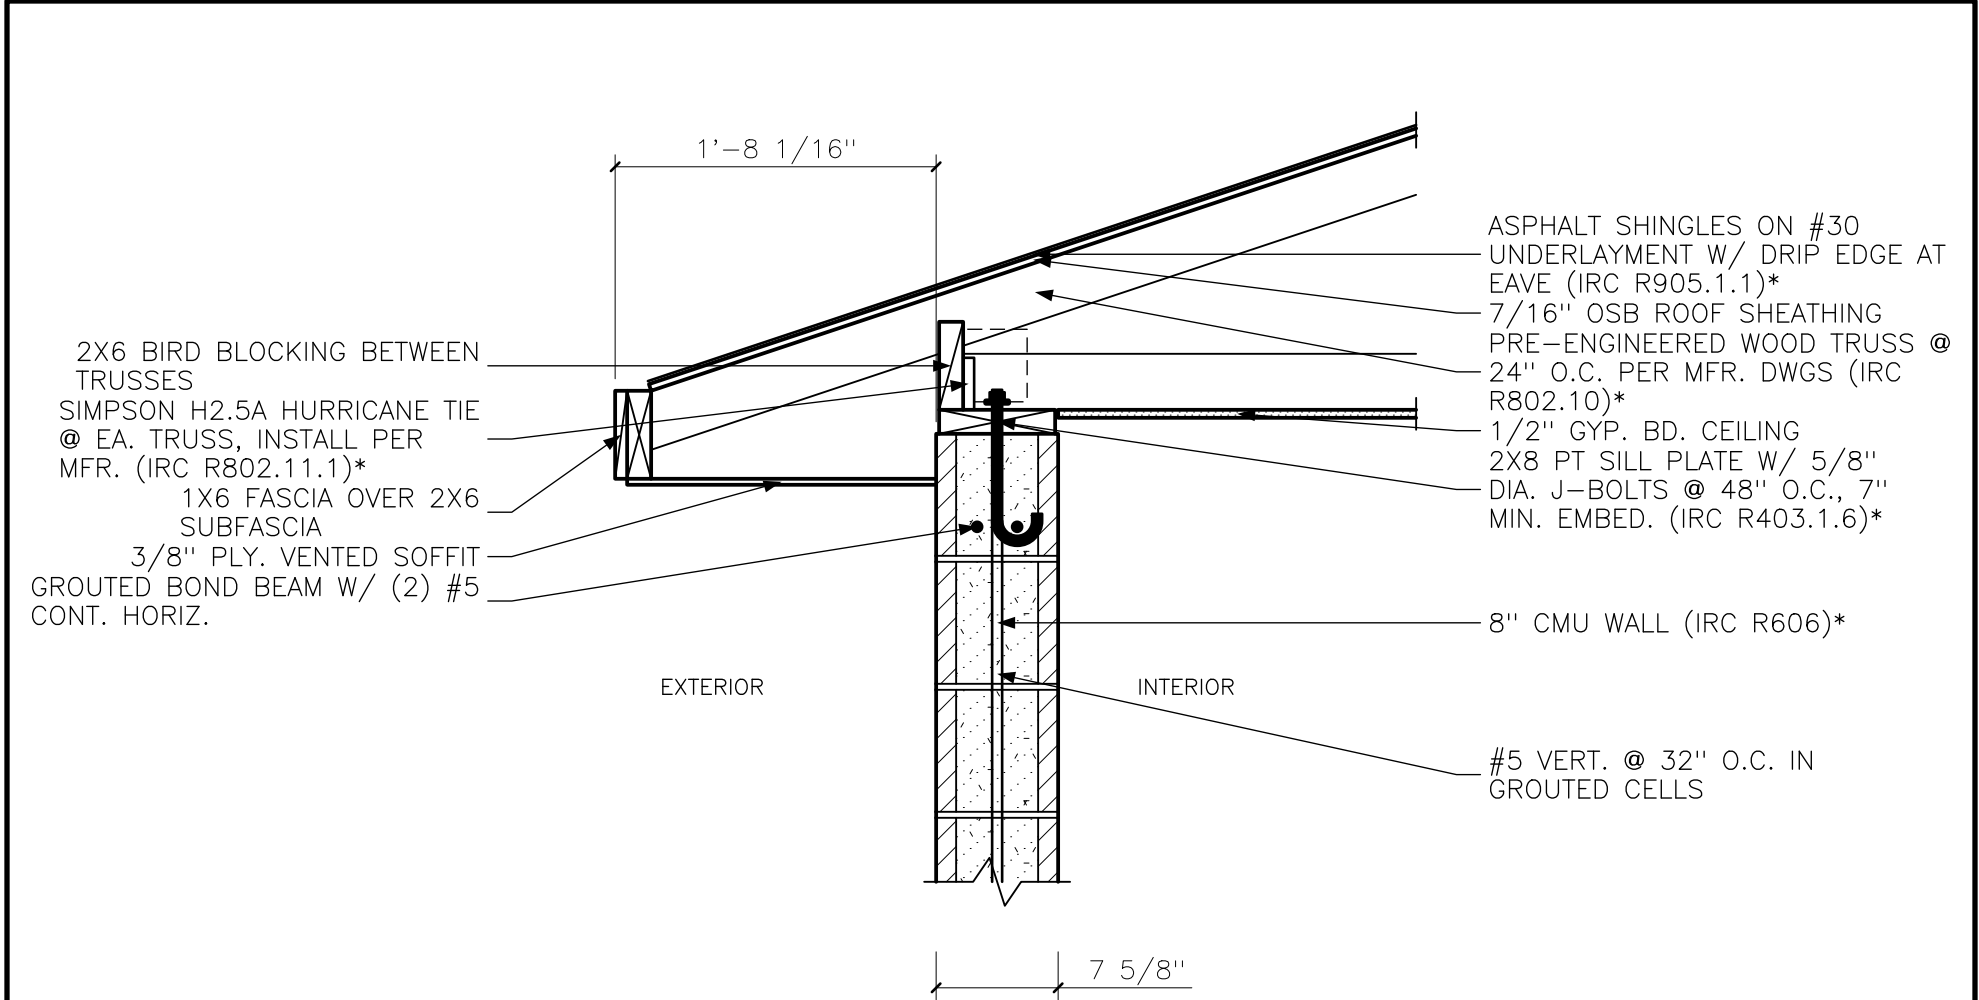


TRUSS BEARING AT CMU WALL

SCALE: 1" = 1'-0"

DETAIL	PROJECT	SCALE	DRAWN	DATE	DETAIL NO
TRUSS BEARING AT CMU WALL		1" = 1'-0"	KERF REFERENCE	2026-10-05	1/S-501