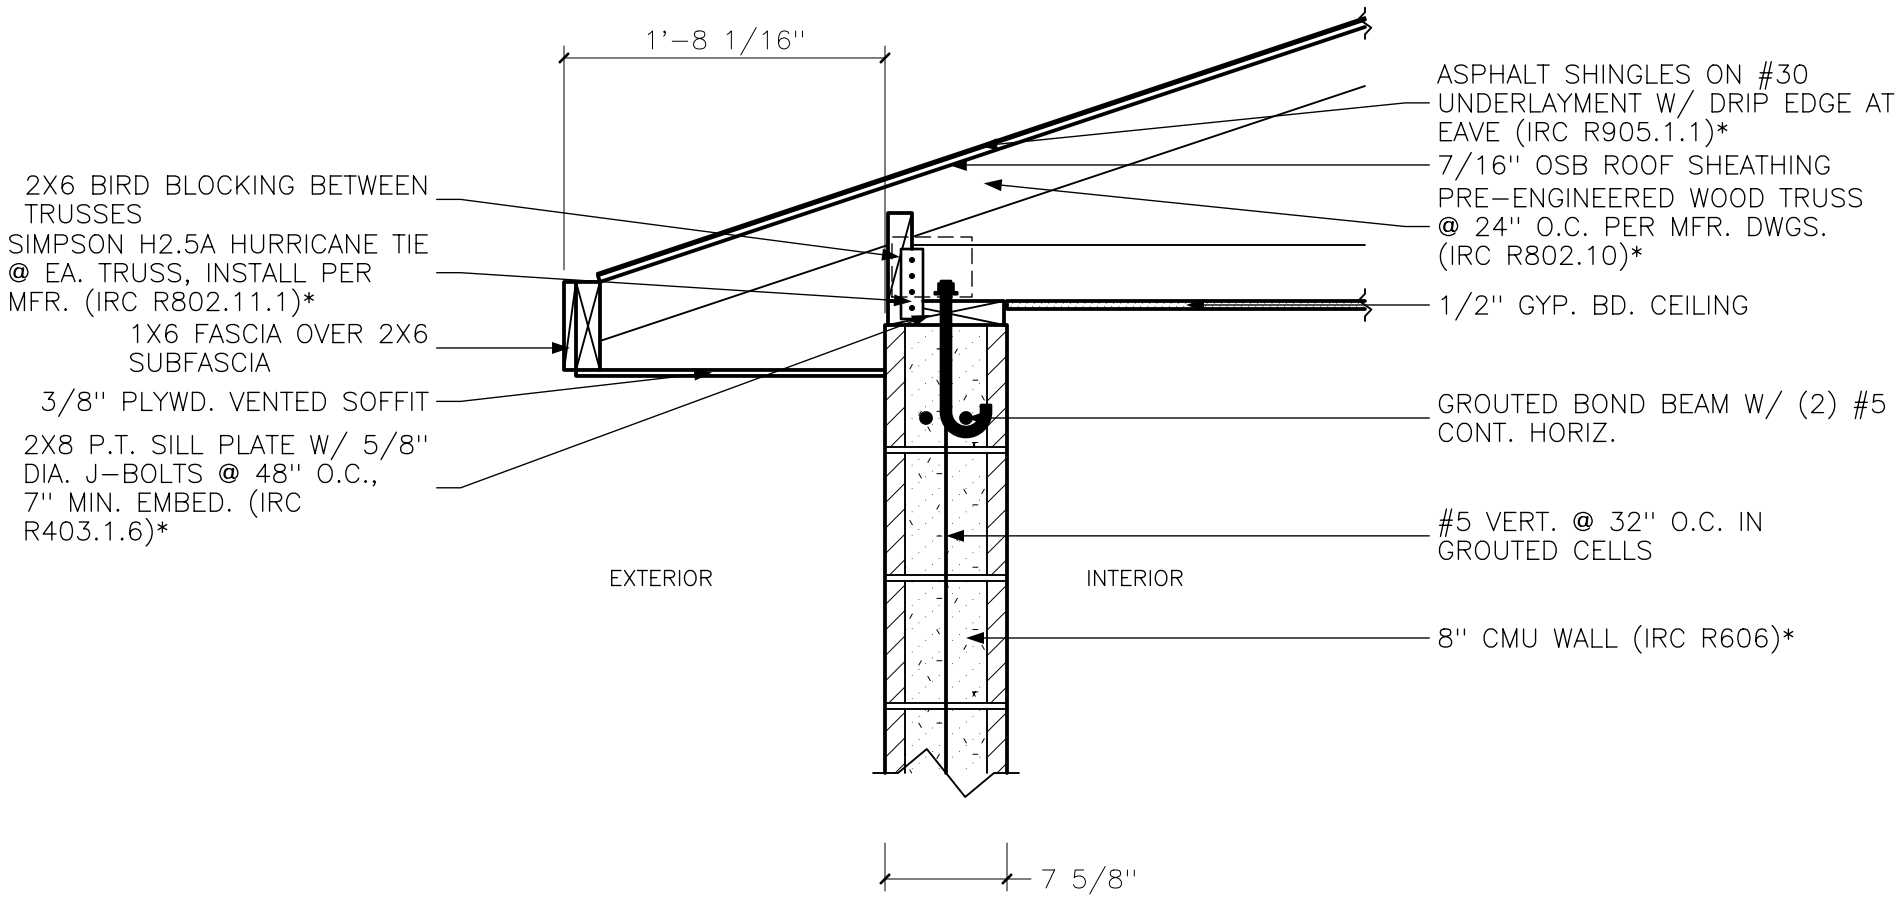


1 / S–501

TRUSS BEARING AT CMU WALL

SCALE: 1" = 1'–0"

DETAIL	PROJECT	SCALE	DRAWN	DATE	DETAIL NO
TRUSS BEARING AT CMU WALL		1" = 1'–0"	KERF REFERENCE	2026–10–05	1/S–501