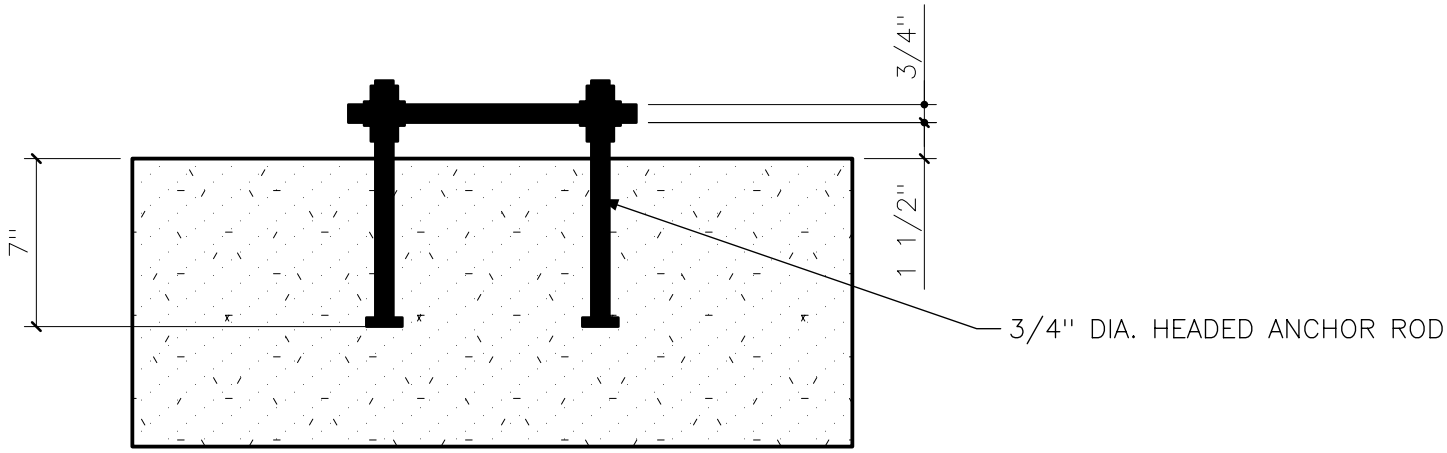


3 SECTION AT ANCHOR RODS

SCALE: 1 1/2" = 1'–0"

DETAIL	PROJECT	SCALE	DRAWN	DATE	DETAIL NO
SECTION AT ANCHOR RODS		1 1/2" = 1'–0"	KERF		3